


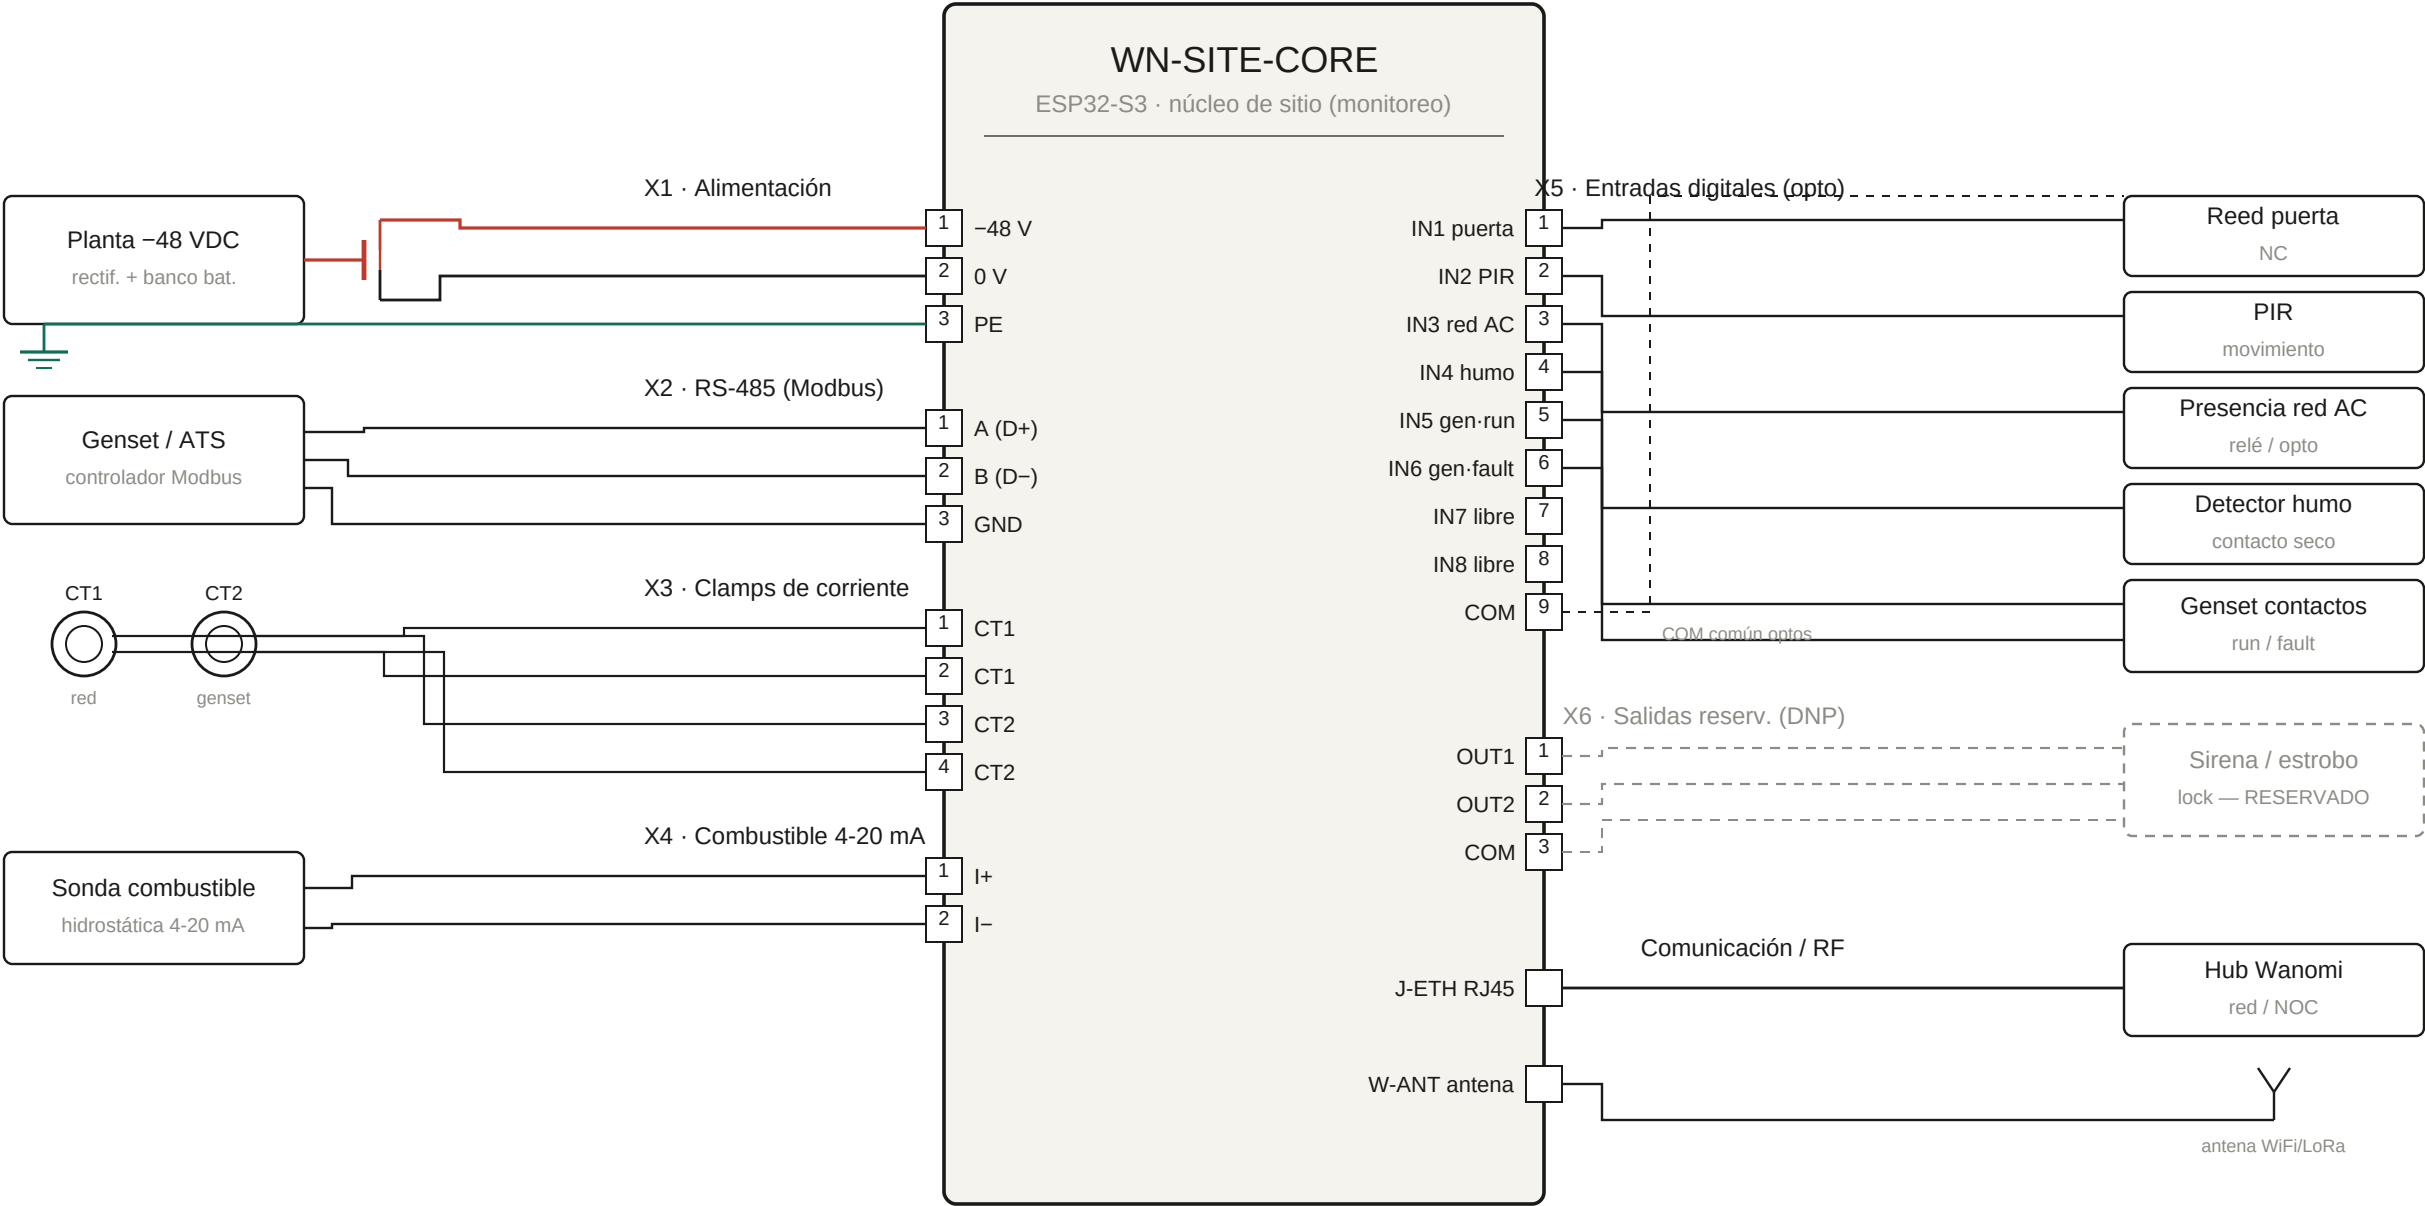

Notas de conexionado

- 1 · Aislación: DC-DC aislado separa masa de campo (-48 V) de masa lógica; RS-485 aislado (ADM2483); entradas por opto.
- 2 · Protecciones: fusible 1 A en -48 V; TVS en entrada DC y líneas de campo; GDT en RS-485 y Ethernet.
- 3 · Cableado: -48 V / 0 V ≥ 1,0 mm². RS-485 y señales: par trenzado apantallado, pantalla a PE en un extremo (CORE).
- 4 · Combustible: lazo 4-20 mA 2 hilos alimentado por el CORE. CT1/CT2: no abrir secundario con primario energizado.
- 5 · X6 (OUT1/OUT2) reservado (DNP), sin poblar en esta instancia. PE = barra de tierra del sitio.

Referencias

- 48 V (energía)
- señal / 0 V
- PE / tierra
- reservado (DNP)

wanomi

Área 3 · Hardware

WN-SITE-CORE

Diagrama de conexionado normalizado

Modo: Monitoreo (Connect+Sense)

Rev: A Fecha: 2026-05-23

Sitio telco · piloto Claro Corrientes

Hoja 1/1 Esc: S/E